


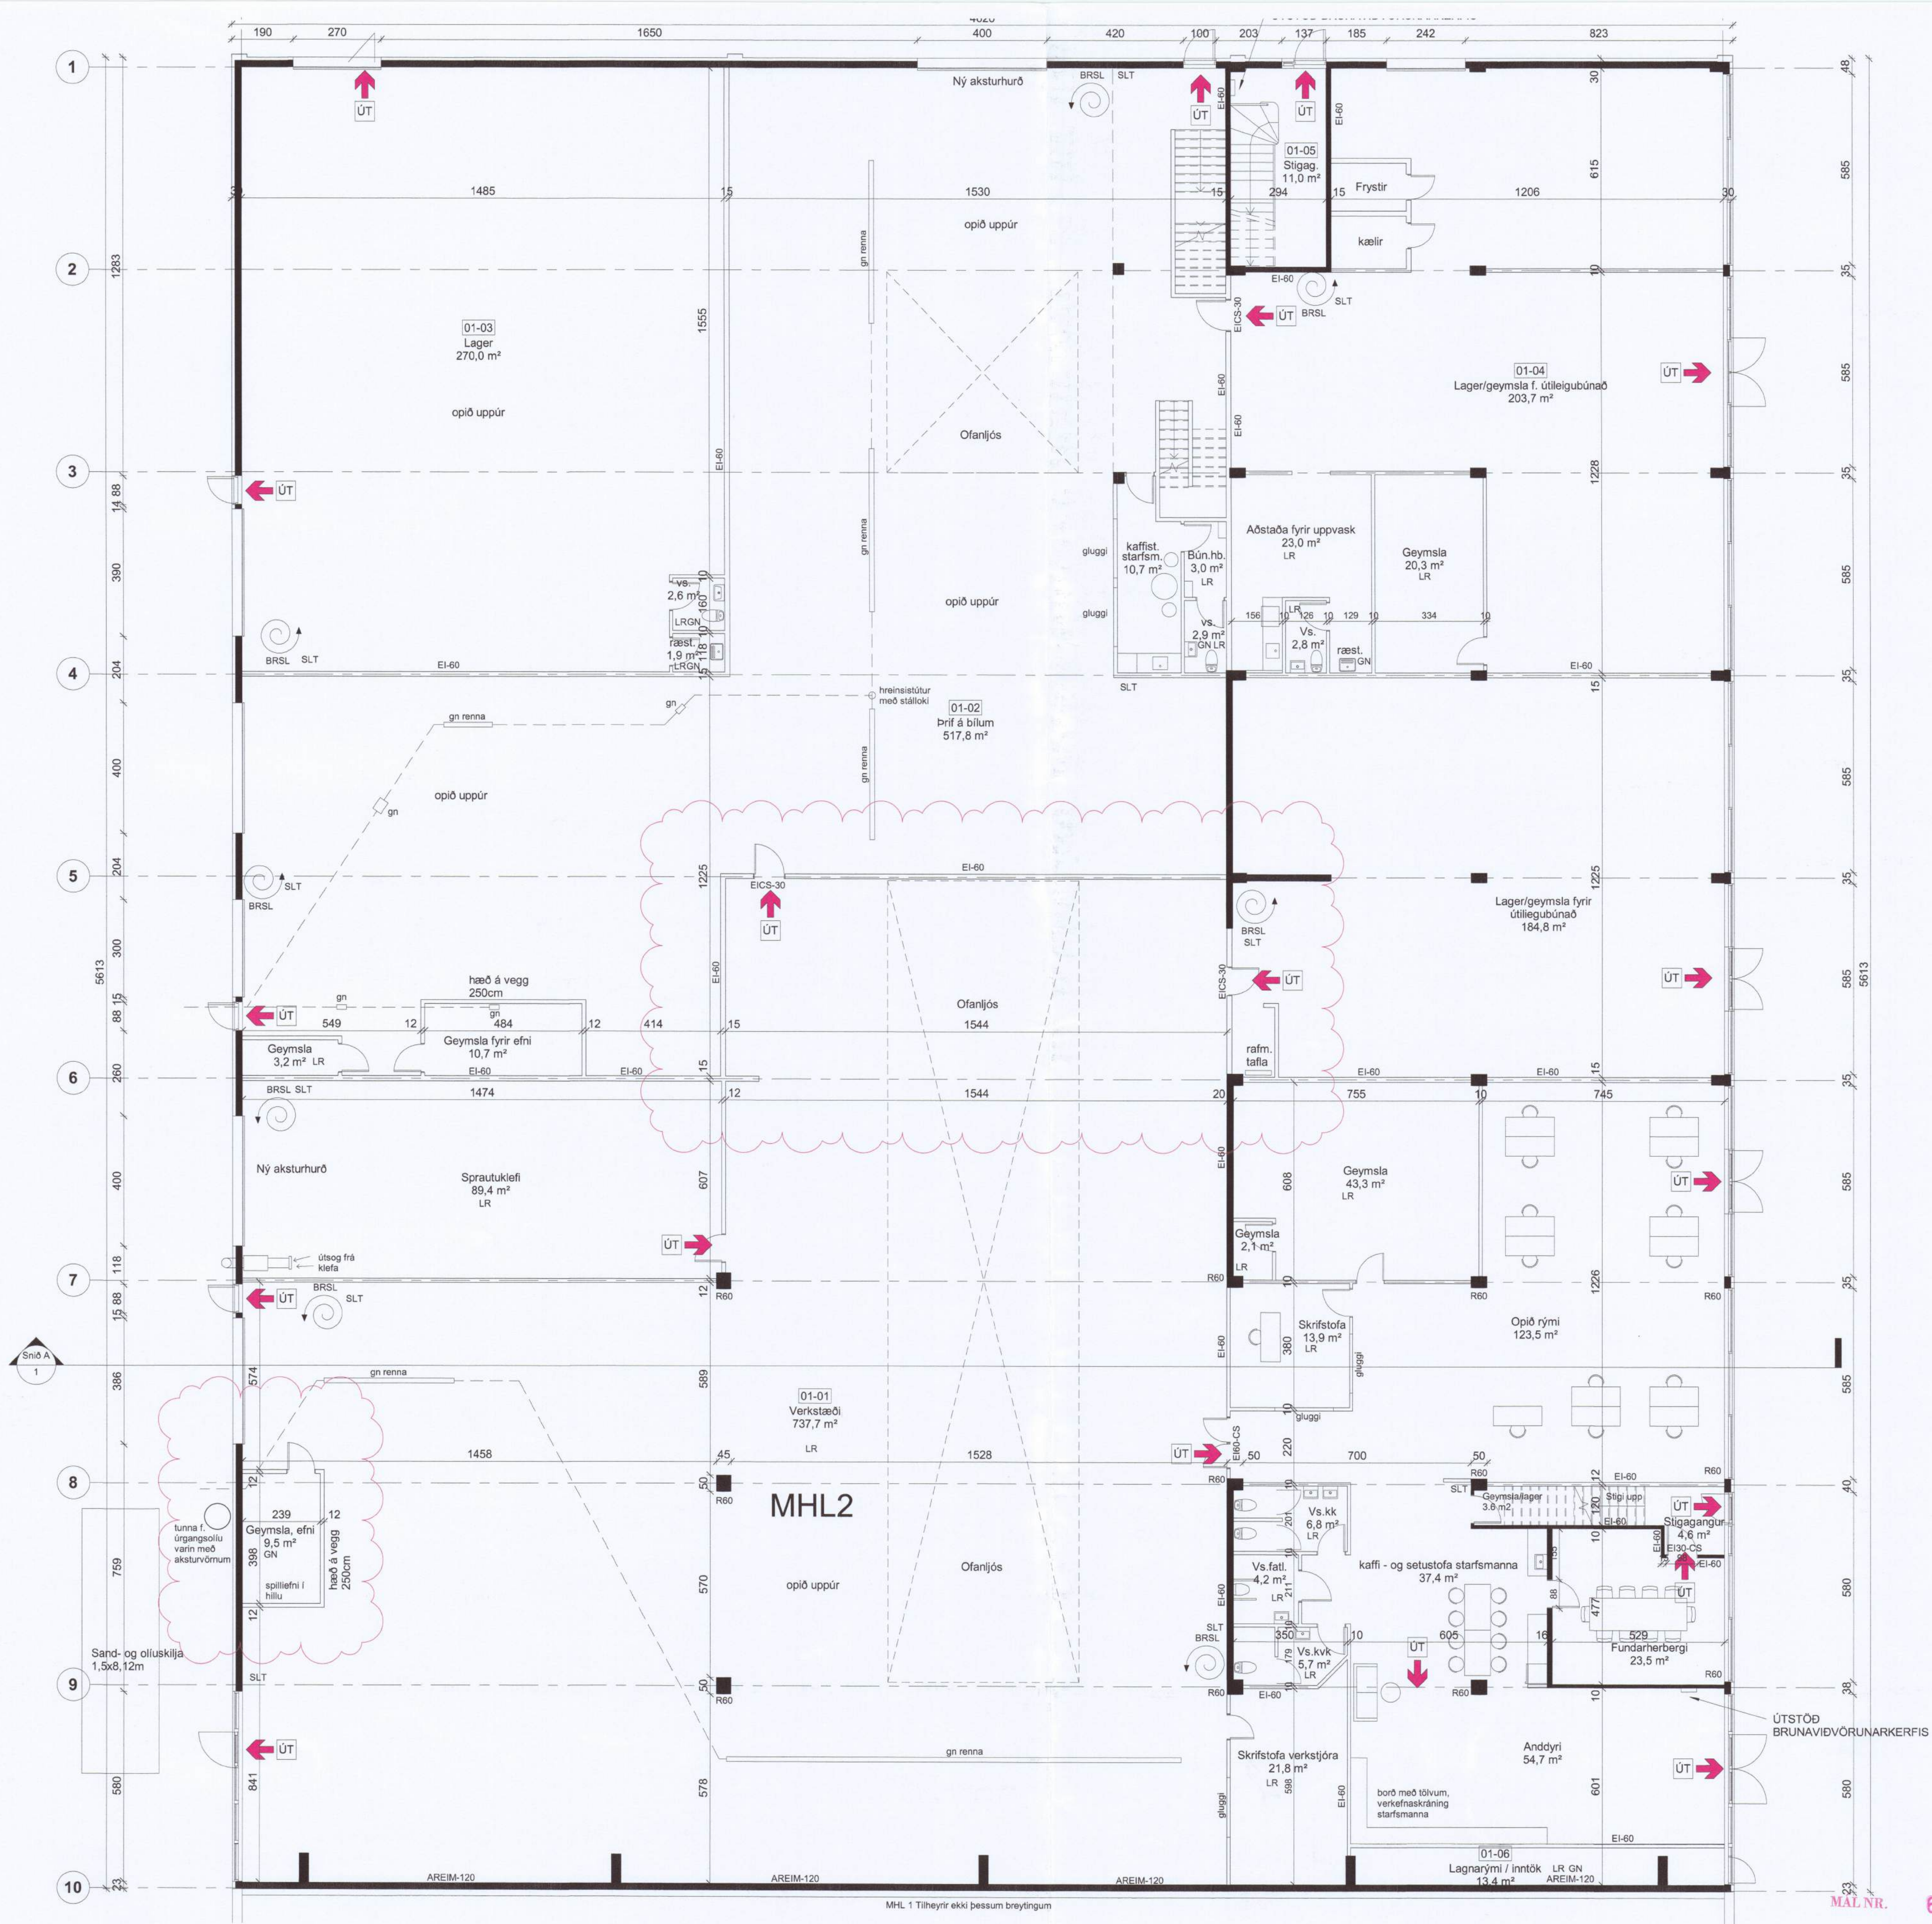

Samþykkt af byggingarfulltrúa með skilyrði

11. OKT. 2022

byggingarfulltrúi

Áskilin lokaúttekt byggingarfulltrúa

Áskilið samþykki heilbrigðiseftirlits

Húsið er upphaflega teiknað af Kristni Sveinbjörnsdóttir byggingarfræðingi með síðari breytingum hjá Gunnlaugi Ó. Johnsson arkitekti og Sigurði Hafsteinssyni byggingateknir.

Breyting B: 16.06.22 - Sótt er um nýtt byggingarleyfi þar sem það eldra er runnið út.

Breyting A: 21.11.19 - verkstæði stækkað, aðstaða fyrir þríf á bilum minnkað, geymsla fyrir efni færð að útvægg. Skráningatalla breytt.

Verkhelti:

Skútuvegur 4

104 Reykjavík

Landnúmer: 105166 Staðgreinir: 0-1- 1420201

Grunnmynd 1.hæð

Hannað af:	AG	Málkvarði:	1: 100
Teiknað af:	AG	Dagsetning:	21.11.19
Samþykkt:		Verknúmer:	10.18

Samþykkt: *M. J. L.*

TAG Teiknistofa

Síðumúla 33 - 108 Reykjavík - KT: 500215-1000

Atli Jóhann Guðbjörnsson - Byggingarfræðingur BFI

Kt: 260978-5789 sími: 568-6681 gsm: 699-4297

atli@tagteiknistofa.is - www.tagteiknistofa.is